



A-A Section

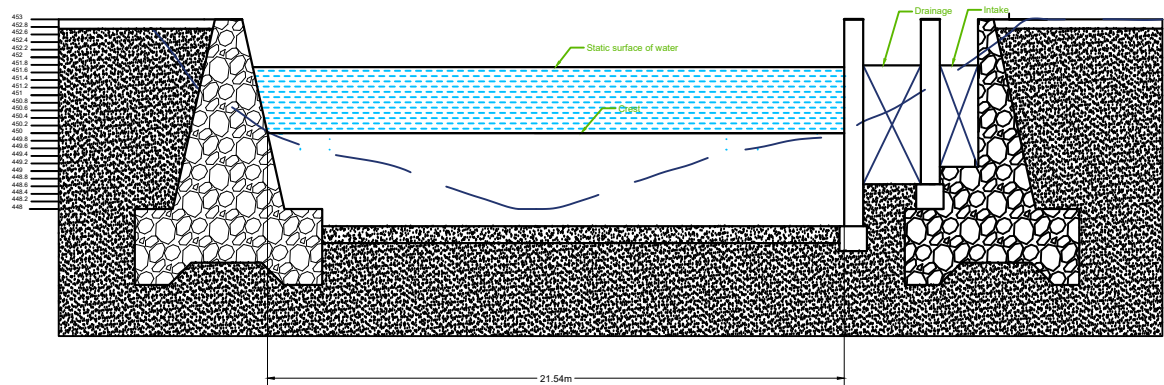


—Scale (All dimensions are in meter)


B-B Section

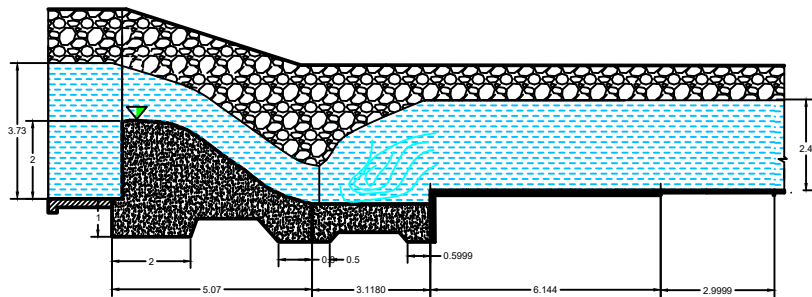

—Scale (All dimensions are in meter)

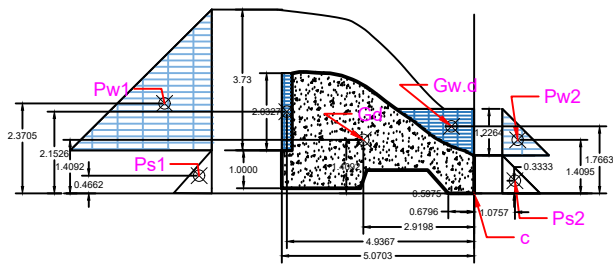


—Scale (All dimensions are in meter)

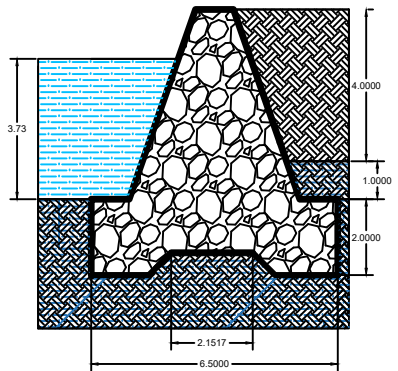


C-C Section

—Scale (All dimensions are in meter)

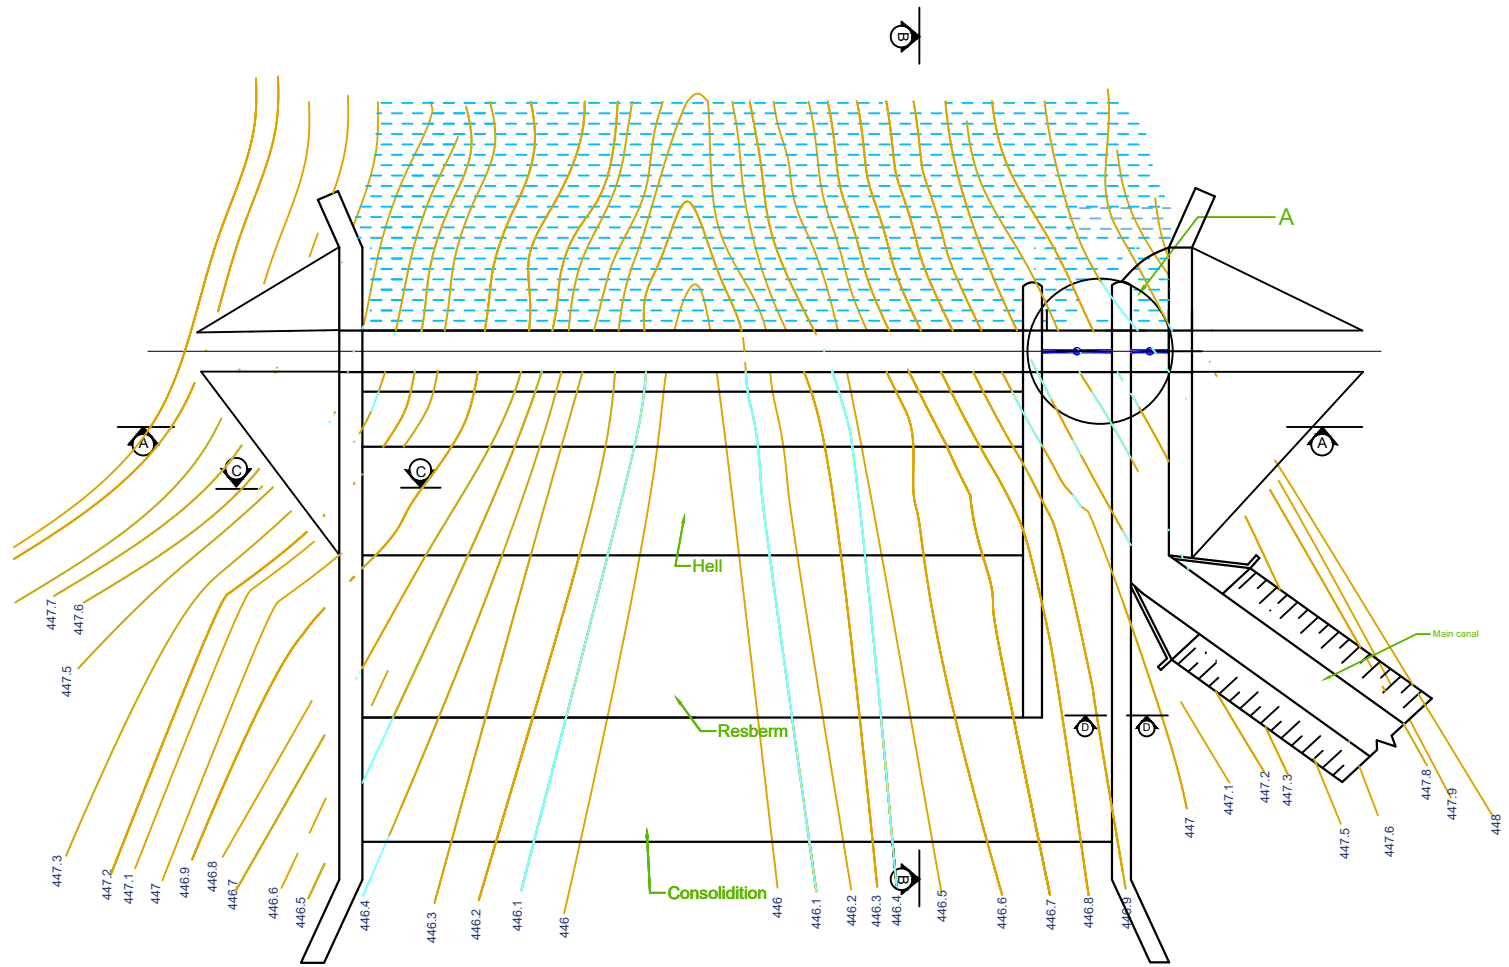

Plan of Dam

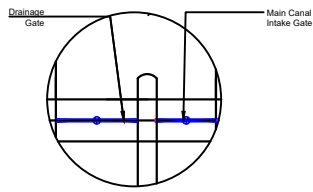

A Details

KPU Kabul Polytechnic University				000	000	004
JOB	Name	Date	Sign	Dam General Plan		
Student	Zahid Rahimyar					
Guidance Teacher	Dr.M.Amwar "Safai"					
Advisor	Dr.M.Amwar "Safai"					
Teacher	Dr.M.Amwar "Safai"					
Head of Department	Dr.M.Amwar "Safai"			Group-HS5-1		
				Sheet	Scale	Mass